根切り図 1/100

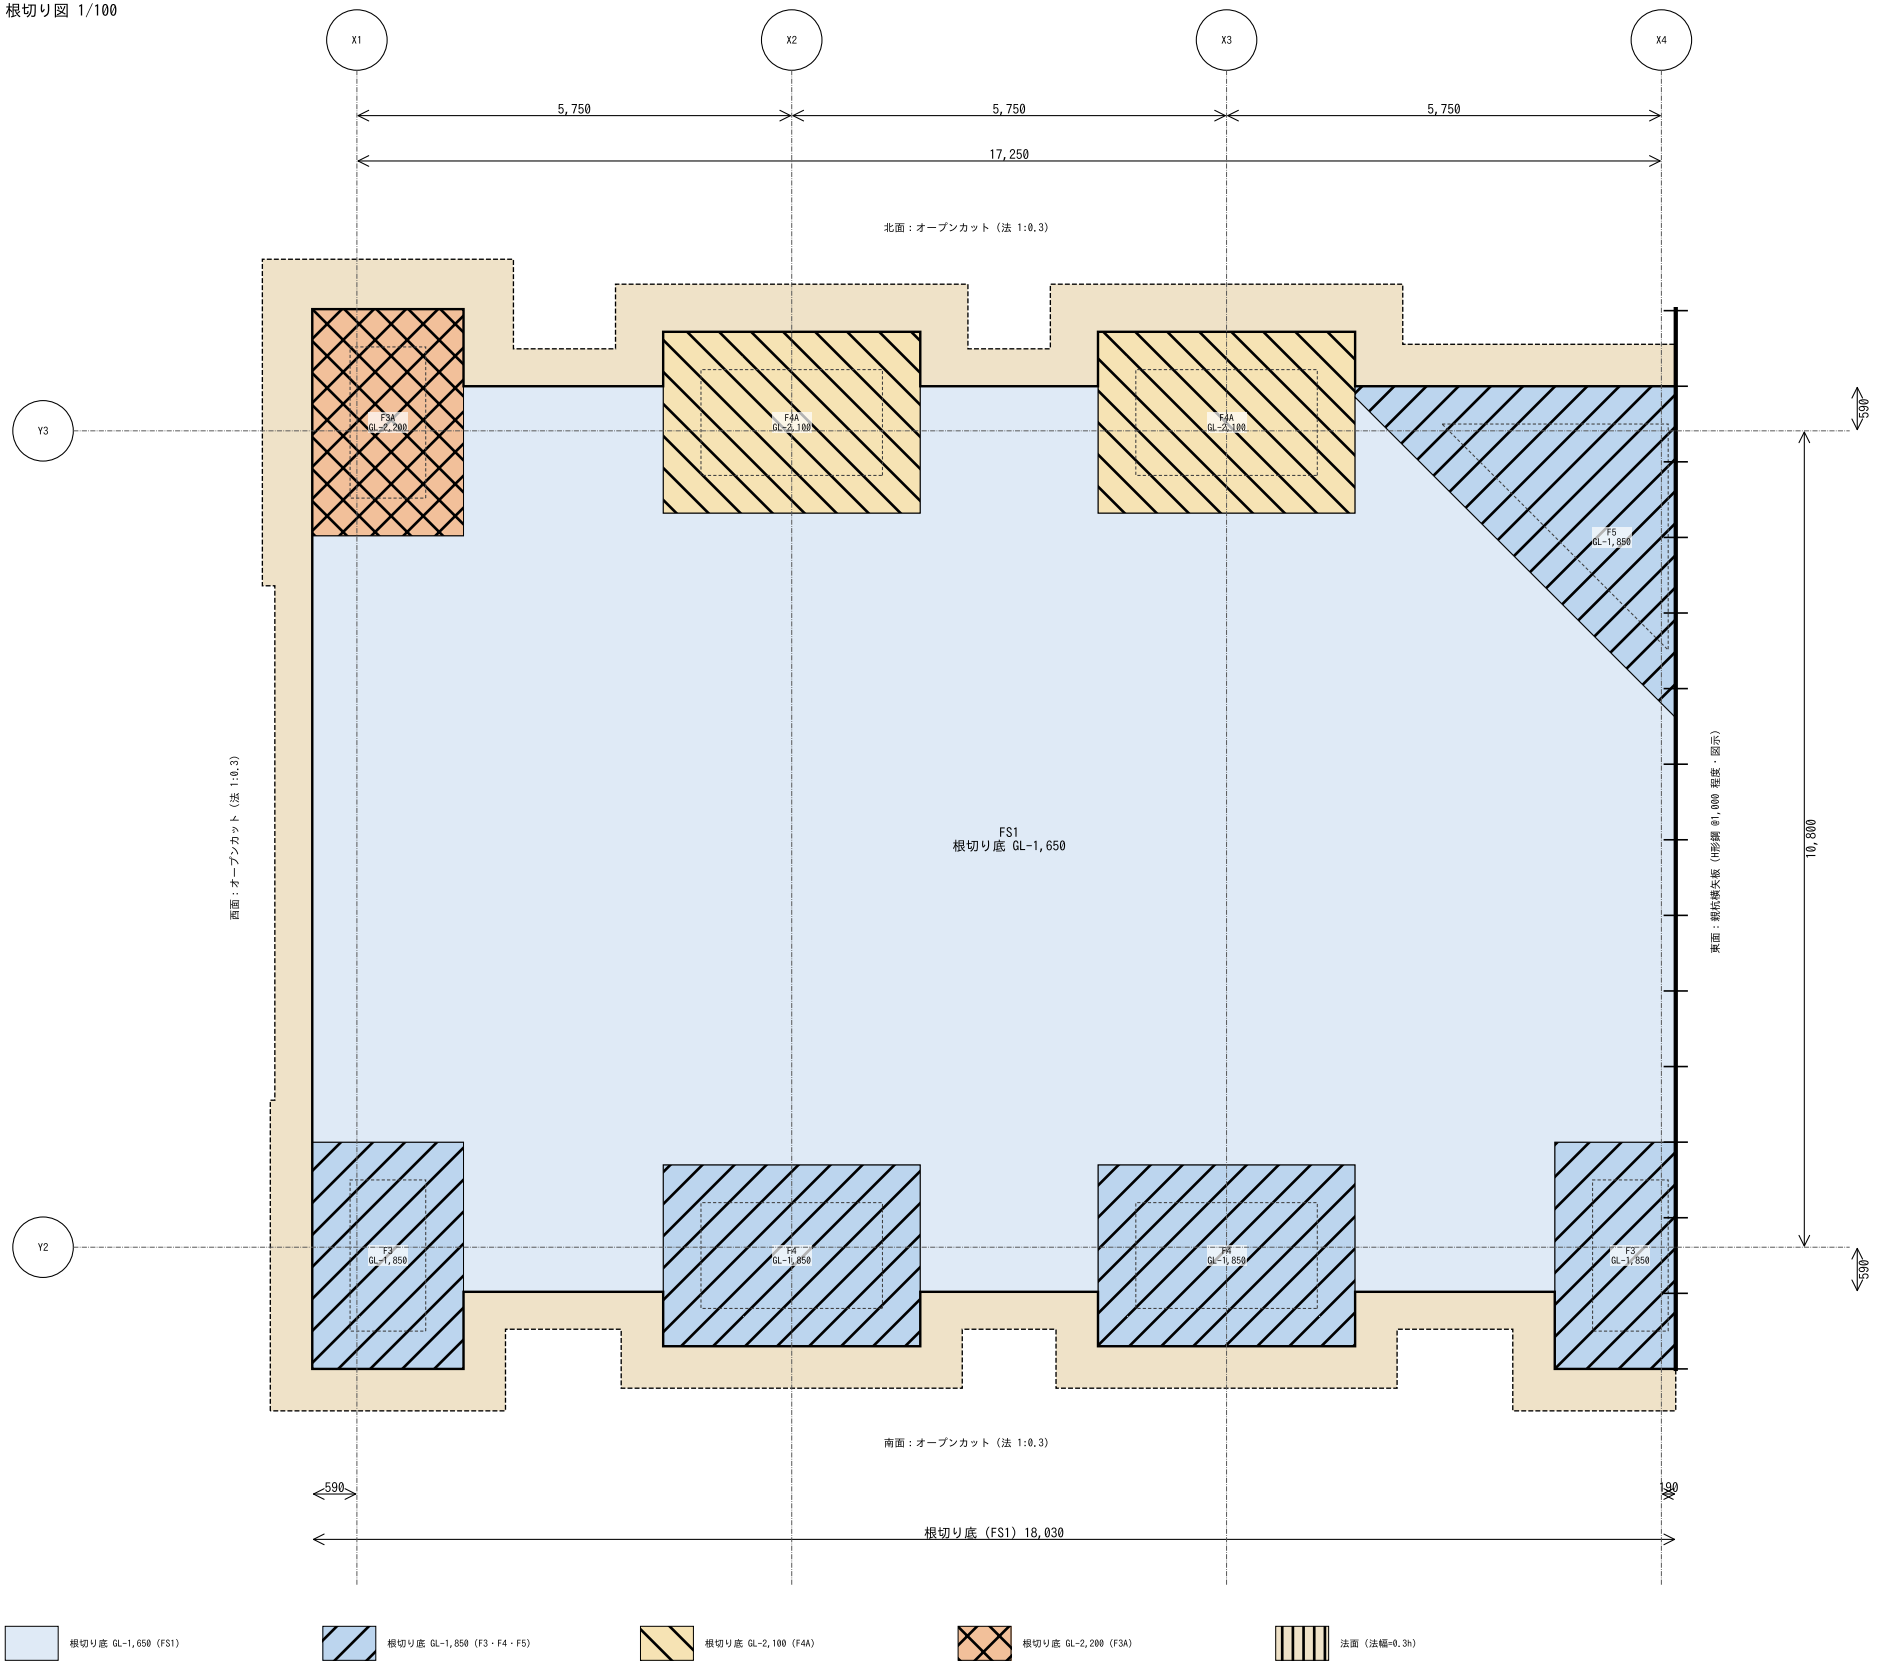
X1
X2
X3
X4
5,750
5,750
5,750
17,250
北面：オープンカット（法 1:0.3）
Y3
Y2
F3A
GL-2,200
F4A
GL-2,100
F4A
GL-2,100
F5
GL-1,850
FS1
根切り底 GL-1,650
F3
GL-1,850
F4
GL-1,850
F4
GL-1,850
F3
GL-1,850
590
590
10,800
西面：オープンカット（法 1:0.3）
東面：親杭横矢板（H形鋼 @1,000 程度・図示）
南面：オープンカット（法 1:0.3）
590
590
根切り底（FS1）18,030
根切り底 GL-1,650（FS1）
根切り底 GL-1,850（F3・F4・F5）
根切り底 GL-2,100（F4A）
根切り底 GL-2,200（F3A）
法面（法幅=0.3h）