

○○寮新築工事 根切図・根切断面図（Y3通り）・掘削土量
【問題】○○寮新築工事の設計図抜粋から根切図と根切断面図（Y3通り）を作図し、根切の掘削土量を算出せよ。ただし山留工法は西面・南面・北面がオープンカット工法、東面は親杭横矢板工法とする。

根切り図 1/100

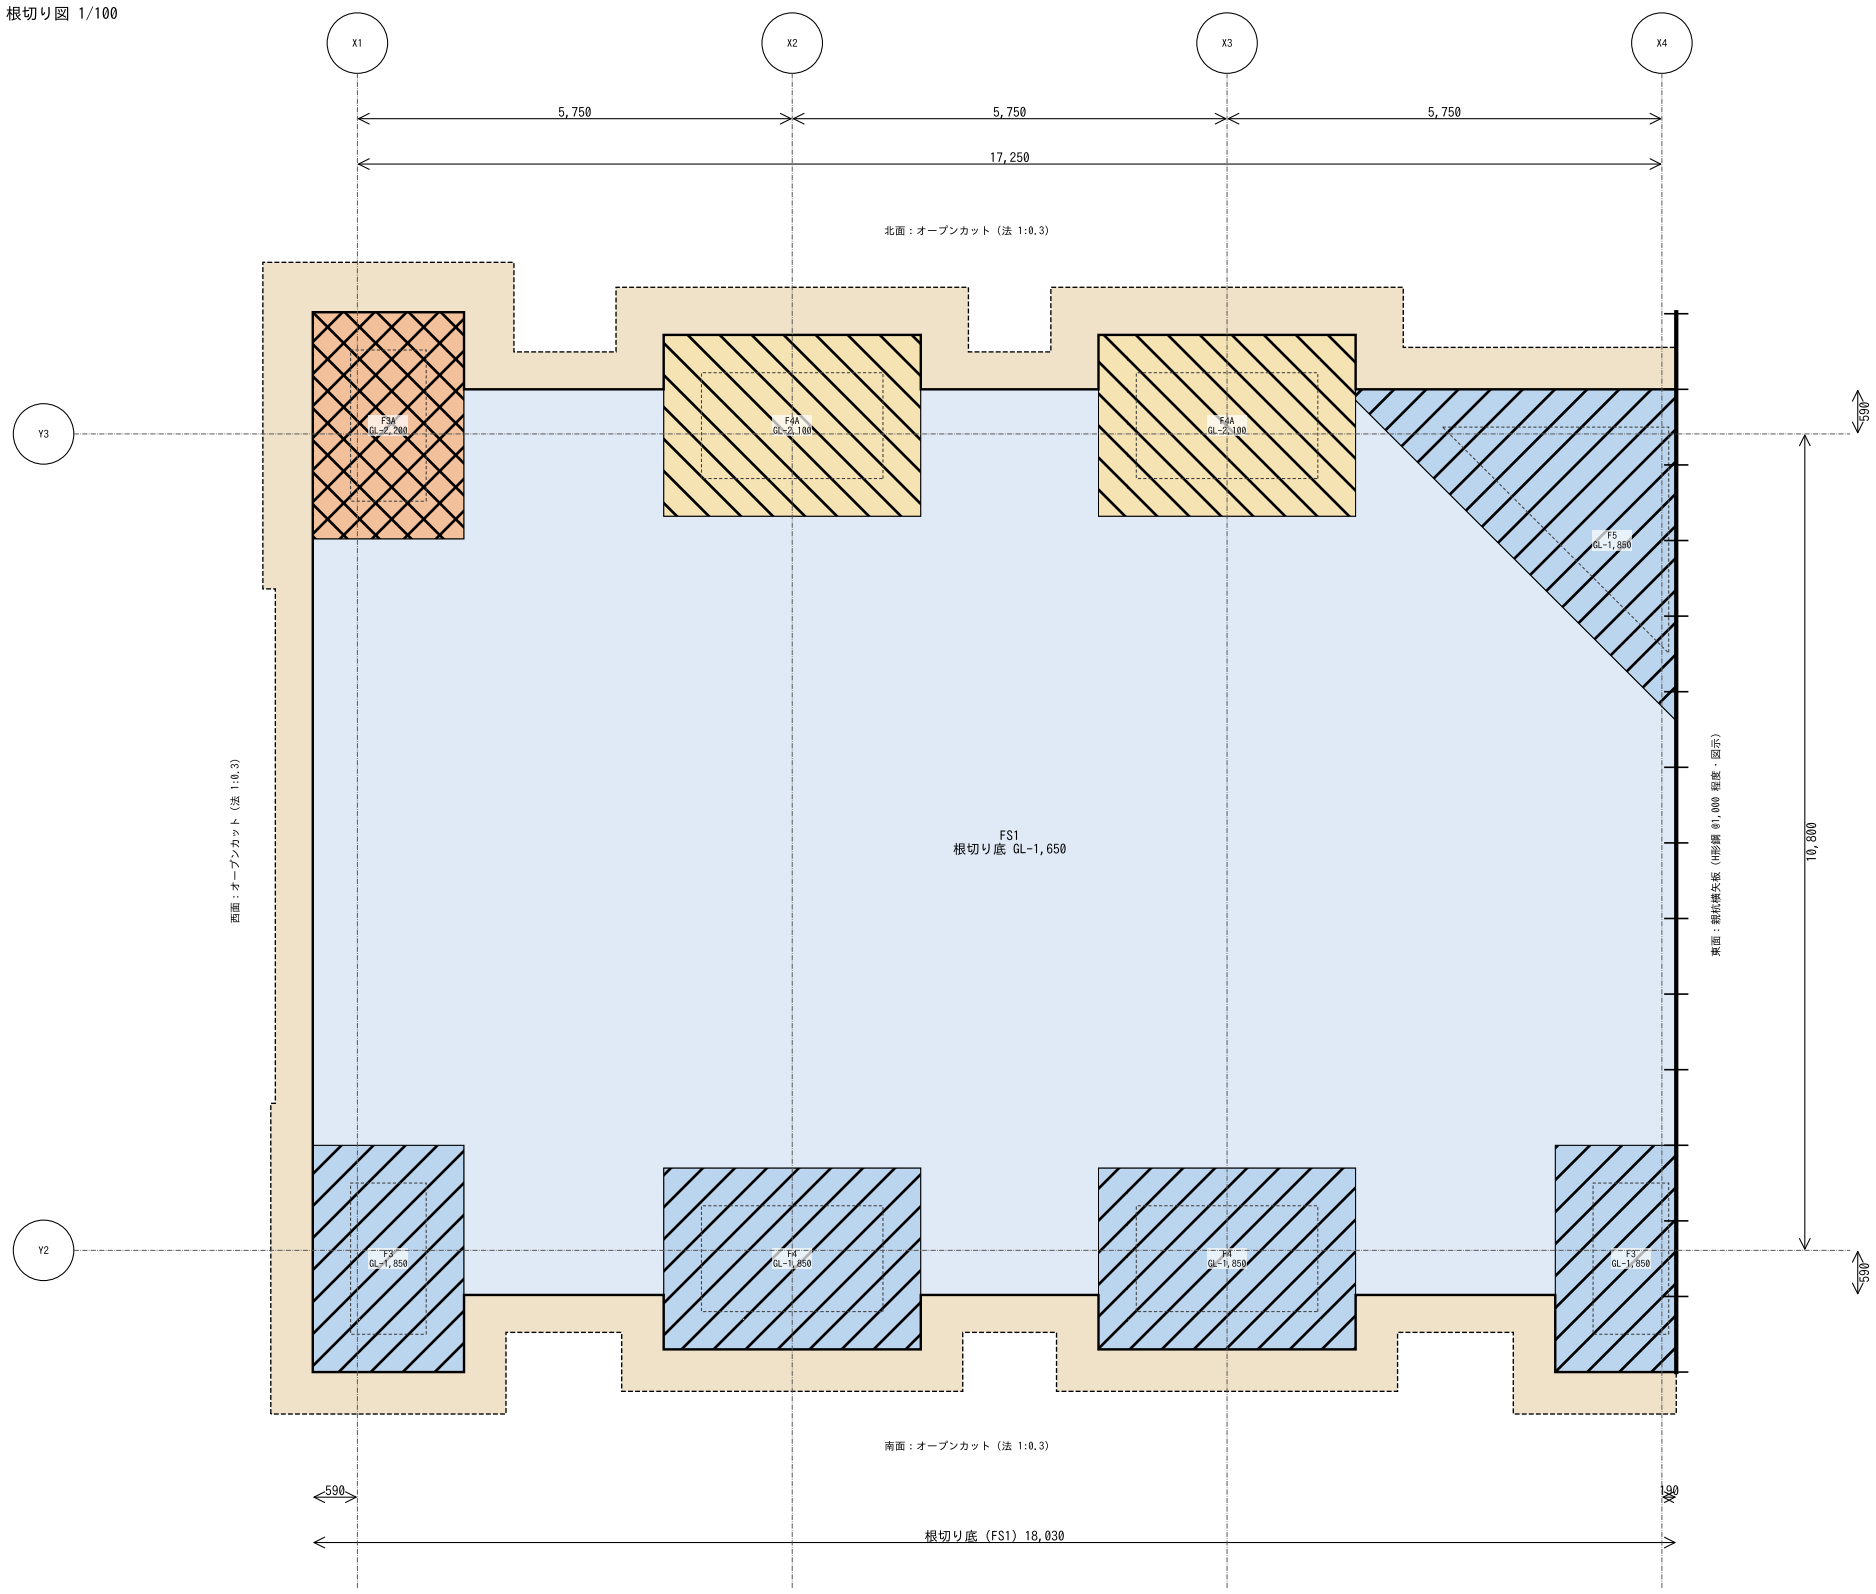

根切り断面図（Y3通り） 1/100

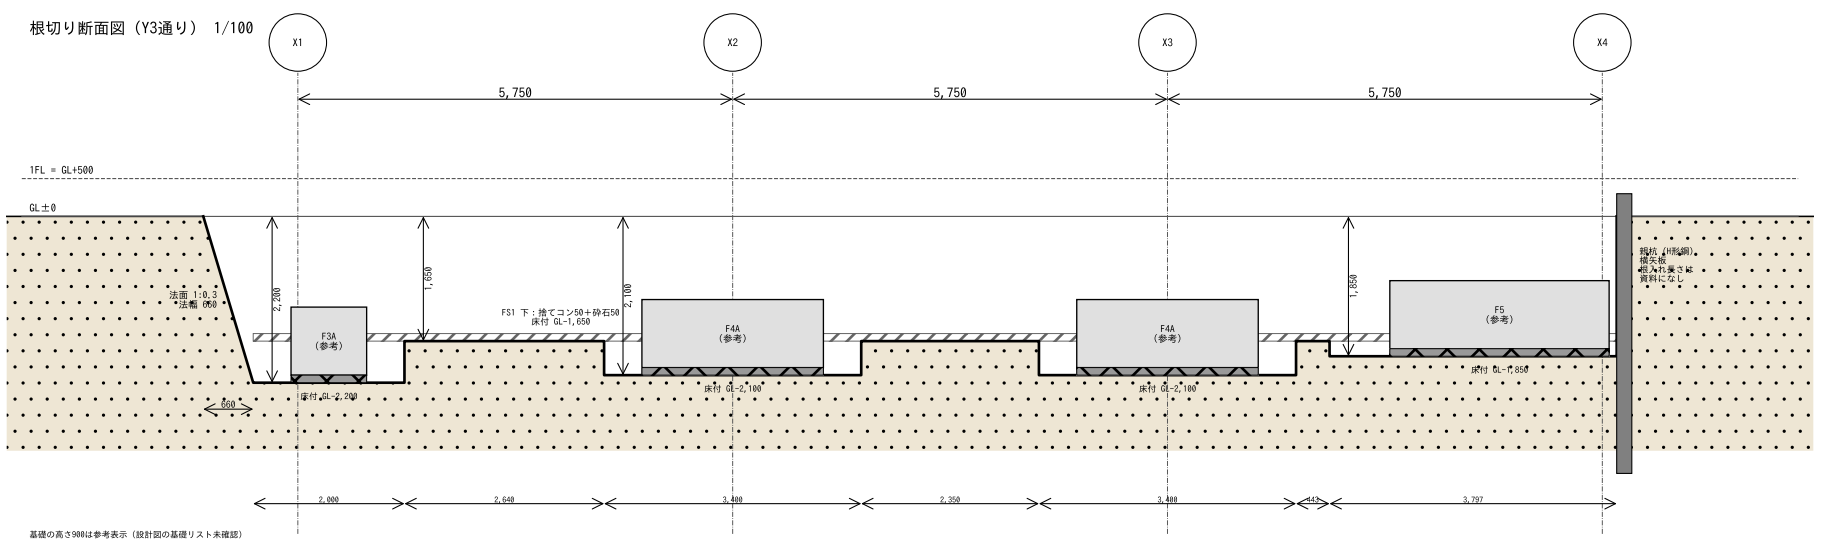

掘削土量　V = 436.27 m³
　方法A　V = Σ(Ai×hi) = 436.266 m³
　方法B　V = A0×1.65 + Σ(Aj×Δhj) = 436.266 m³　（A0 = 248.282 m²）
　余幅 = 作業のゆとり幅0.5m + 法幅(0.3h)/2、東面（親杭横矢板）は余幅0.1m・法なし

注: 寸法は授業スライド・授業中の着色根切図・課題用紙の写真から読取り・導出。F3A平面寸法・外周梁外面位置は仮定（08_未解決事項.md）。元の課題PDFへの書込み版は未作成。