根切り断面図（Y3通り） 1/100

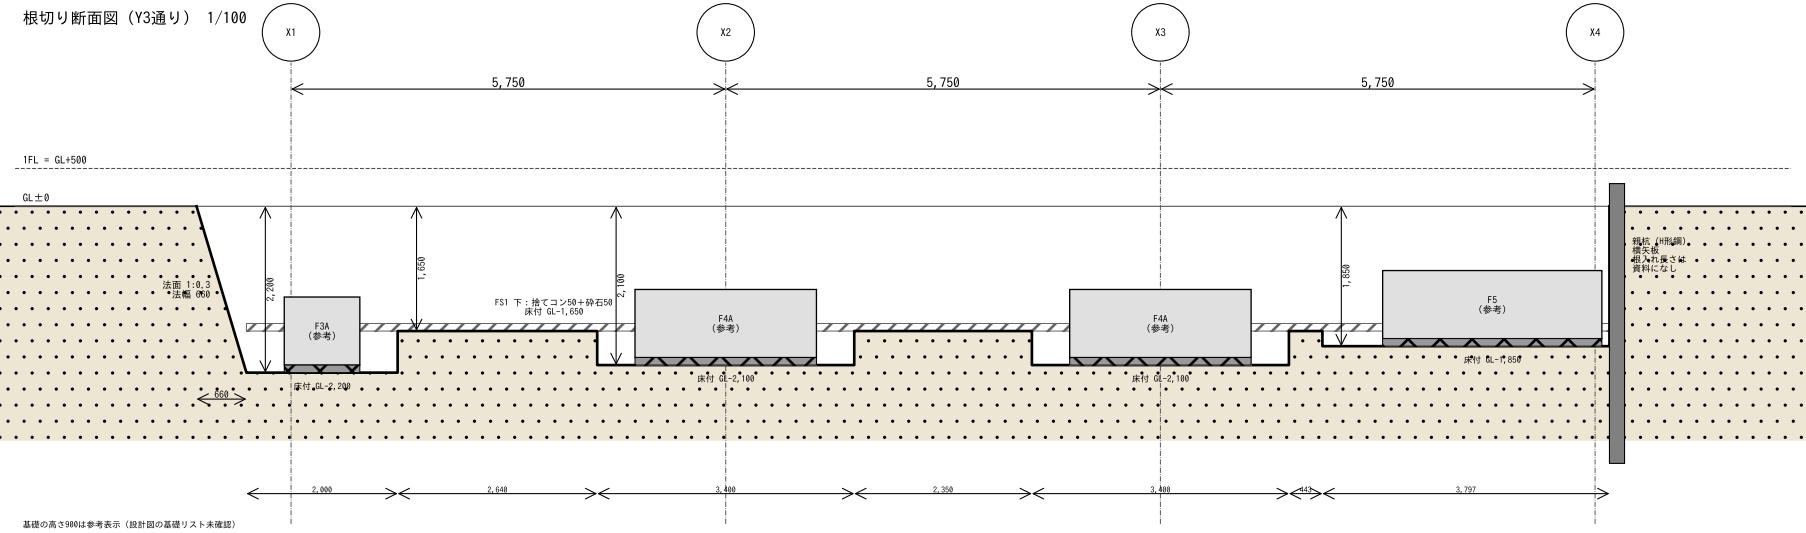

基礎の高さ900は参考表示（設計図の基礎リスト未確認）